

PRV-101,PRV-102
AND PRV-103

PRESSURE RELIEF
VALVE

EVP-101, EVP-102
AND EVP-103


EFFECTS OF
EVAPORATOR

V-101 AND V-102

GLOBE VALVES

P-101 AND P-102

CENTRIFUGAL PUMPS

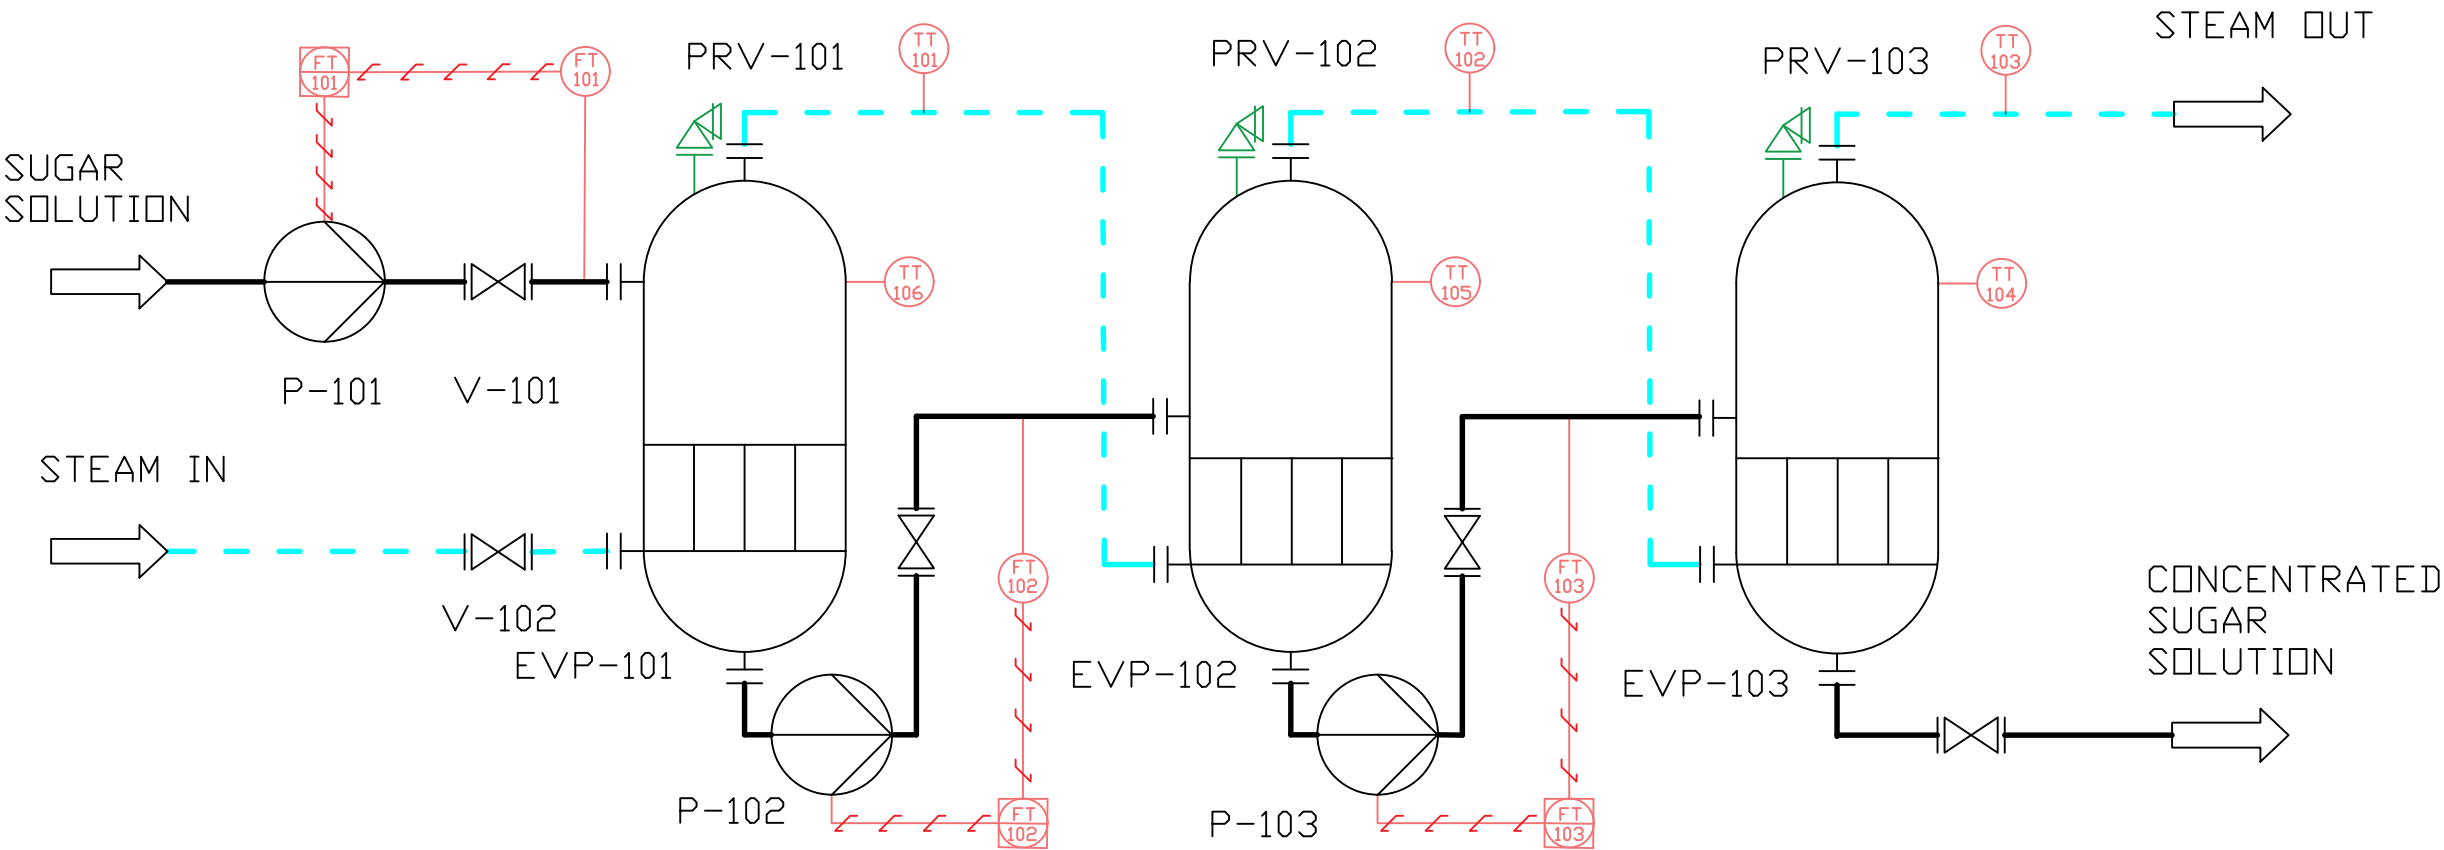

SENSORS, TRANSMITTERS AND
CONTROLS

FT	FLOW TRANSMITTER
TT	TEMPERATURE TRANSMITTER
FIC	FLOW INDICATOR CONTROLLER

General Notes

Standard:
BS EN ISO
10628-2:2012

STEAM

CONTROLS

SAFETY

ELECTRICAL
SIGNAL

STREAM

No.	Revision/Issue	Date

Firm Name and Address

Samarpan Mani
Gautam

Project Name and Address
Sugar Production
Plant
Piping and
Instrumentation
Diagram

Sheet	01
Date	2026-04-30
Scale	1:1

